
ПРИЛОЖЕНИЕ 10


Инженерно-геологический разрез по линии I-I

Масштаб: горизонтальный 1:500, вертикальный 1:100

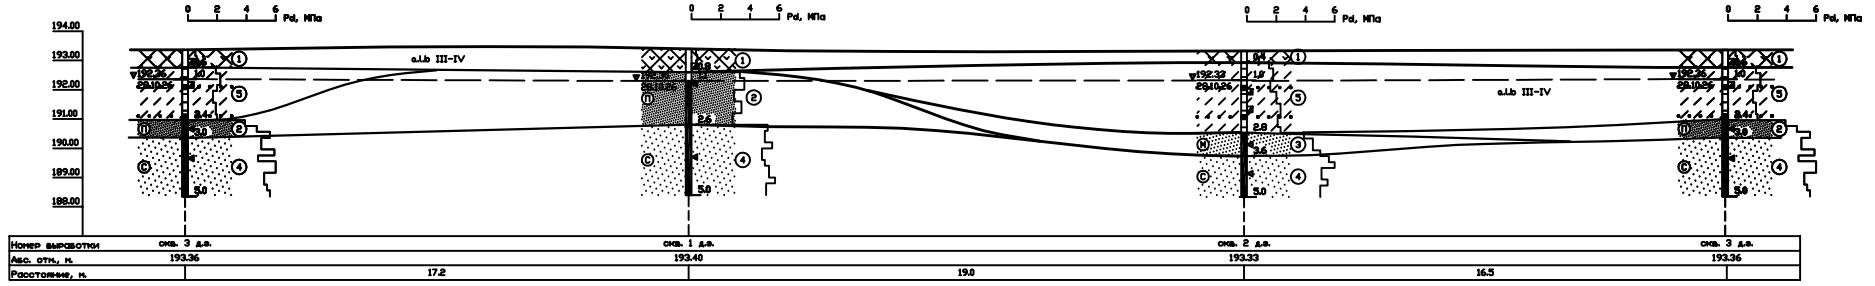

Инженерно-геологический разрез по линии II-II

Масштаб: горизонтальный 1:500, вертикальный 1:100

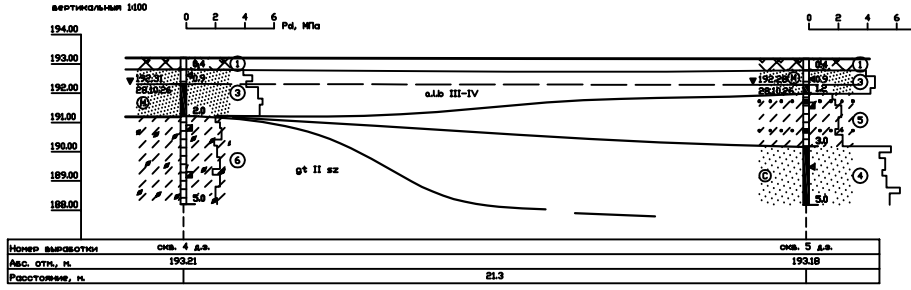

Условные обозначения

1. Литология
   - сильнозаторфованный грунт
   - (С) песок средний
   - (М) песок мелкий
   - (П) песок пылеватый
   - супесь пылеватая
   - супесь моренная
   - прослойки песка
2. Места отбора образцов, проб
   - грунта нарушенного сложения
   - грунта ненарушенного сложения для определения физических свойств
3. Обозначения по скважине
   - ▽ 192.36 / 28.10.26 — установившийся уровень воды, его абс.отм.,м,дата замера,глубина,м
   - водонасыщенный грунт
   - глинистый грунт, содержащий воду в отдельных, маломощных линзах и прослойках песка
   - 5,0 — глубина подошвы слоя, ИГЭ, забоя скважины,м
4. Консистенция
   - маловлажный грунт
   - влажный грунт
   - пластичная
5. Графики зондирования
   - динамического
   - статического: Pd, МПа (0 2 4 6)
   - шкалы и графики зондирования грунтов
6. Границы
   - 1 стратиграфическая и генетическая
   - 2 установленная(1) и предполагаемая(2)
   - литологическая установленная
   - литологическая предполагаемая
7. Прочие
   - a,l,b III-IV — стратиграфический индекс
   - (2) — номер инженерно-геологического элемента
   - I-I — номер инженерно-геологического разреза
   - ДЗ — точки статического зондирования

Колич.	Лист	Nдок.	Подпись	Дата
Геолог	Шалобода			10.26
Проверил	Шалобода			10.26

10.28.2026

Строительство одноквартирного жилого дома по адресу Минская область, Минский район, Колодищанский с/с, д. Глебковичи, ул. Авиаторская, 22

Разведочное бурение

СТАДИЯ	ЛИСТ	ЛИСТОВ
С	2	

Инженерно-геологический разрез по линии I-I

ООО "ИНТГЕО"