ПРИЛОЖЕНИЕ 10

Инженерно-геологический разрез по линии I-I

Масштаб: горизонтальный 1:500
вертикальный 1:100

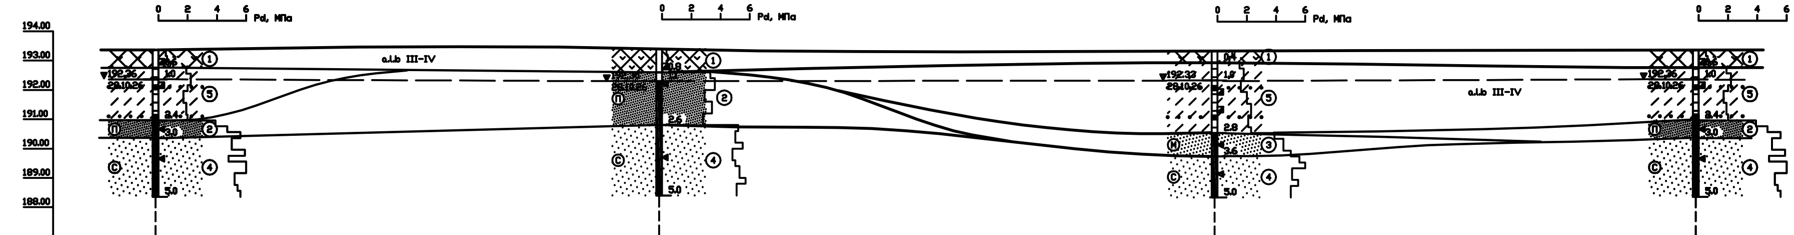

Номер выработки	скв. 3 д.в.	скв. 1 д.в.	скв. 2 д.в.	скв. 3 д.в.
Абс. отм., м.	193.36	193.40	193.33	193.36
Расстояние, м.	17.2	19.0	16.5	

Инженерно-геологический разрез по линии II-II

Масштаб: горизонтальный 1:500
вертикальный 1:100

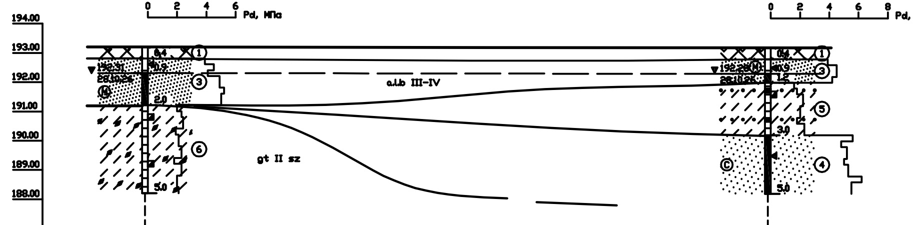

Номер выработки	скв. 4 д.в.	скв. 5 д.в.
Абс. отм., м.	193.21	193.18
Расстояние, м.	21.3	

Условные обозначения

1. Литология

- ▨ сильнозаторфованный грунт
- Ⓒ песок средний
- Ⓜ песок мелкий
- Ⓟ песок пылеватый
- ▨ супесь пылеватая
- ▨ супесь моренная
- ⋯ прослойки песка

2. Места отбора образцов, проб

- грунта нарушенного сложения
- грунта ненарушенного сложения для определения физических свойств

3. Обозначения по скважине

- маловлажный грунт
- влажный грунт
- 192.36 / 28.10.26 установившийся уровень воды, его абс.отм.,м,дата замера,глубина,м
- водонасыщенный грунт
- глинистый грунт, содержащий воду в отдельных, маломощных линзах и прослойках песка
- 5,0 глубина подошвы слоя, ИГЭ, забоя скважины,м

4. Консистенция

- пластичная

5. Графики зондирования

динамического

0 2 4 6 Pd, МПа

шкалы и графики зондирования грунтов

6. Границы

- 1 стратиграфическая и генетическая
- 2 установленная(1) и предполагаемая(2)
- литологическая установленная
- литологическая предполагаемая

7. Прочие

- a.l.b III-IV стратиграфический индекс
- ② номер инженерно-геологического элемента
- I-I номер инженерно-геологического разреза
- Д3 точки статического зондирования

	Колич	Лист	Nдок.	Подпись	Дата	10.28.2026
						Строительство одноквартирного жилого дома по адресу: Минская область, Минский район, Колодищанский с/с, д. Глебковичи, ул. Абрикосовая, 22
Геолог		Шалабода			10.26	Разведочное бурение — СТАДИЯ: С; ЛИСТ: 2; ЛИСТОВ:
Проверил		Шалабода			10.26	Инженерно-геологический разрез по линии I-I — ООО "ИНТГЕО"