

Ситуационнаясхема

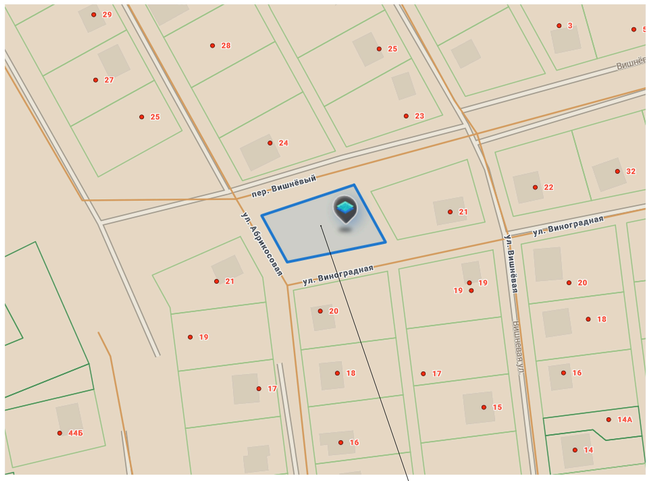

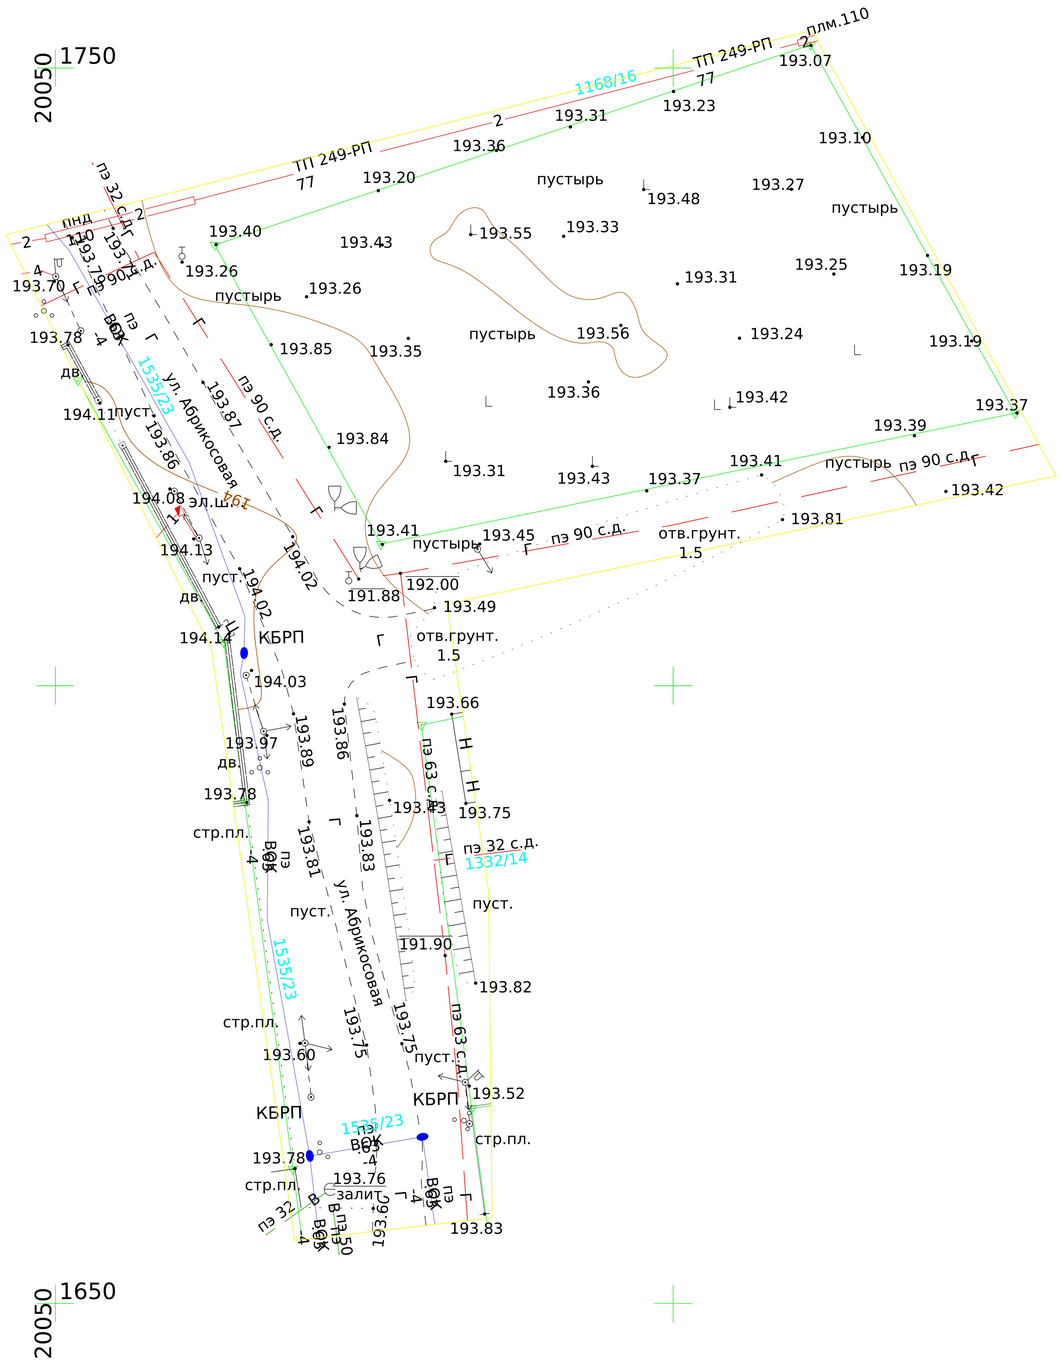

Система координат г. Минск
Система высот Балтийская

з-з. 5656 от 21.10.26 г.

пл.:+1+20_5

S-0.35

						Объект № 22.10-26 ИЗ		
						Инженерные сети жилого дома, расположенного по адресу: Минская обл., Минский р-н, Колодищанский с/с, д. Глебковичи, ул. Абрикосовая, 22		
Изм.	Кол.уч.	Лист	№ док	Подпись	Дата			
						Заказчик : домовладелец	Стадия	Лист / Листов
Руководитель		Сытько Д.М.			07.25			1 / 1
Исполнит.		Жизневский А. Я.			07.25			
Чертил		Степанюк О. В.			07.25	Топографический план М 1:500 Высота сечения рельефа 0.5 м	ООО ТопДиАл +375(29)1195974 +375(29)3088553	