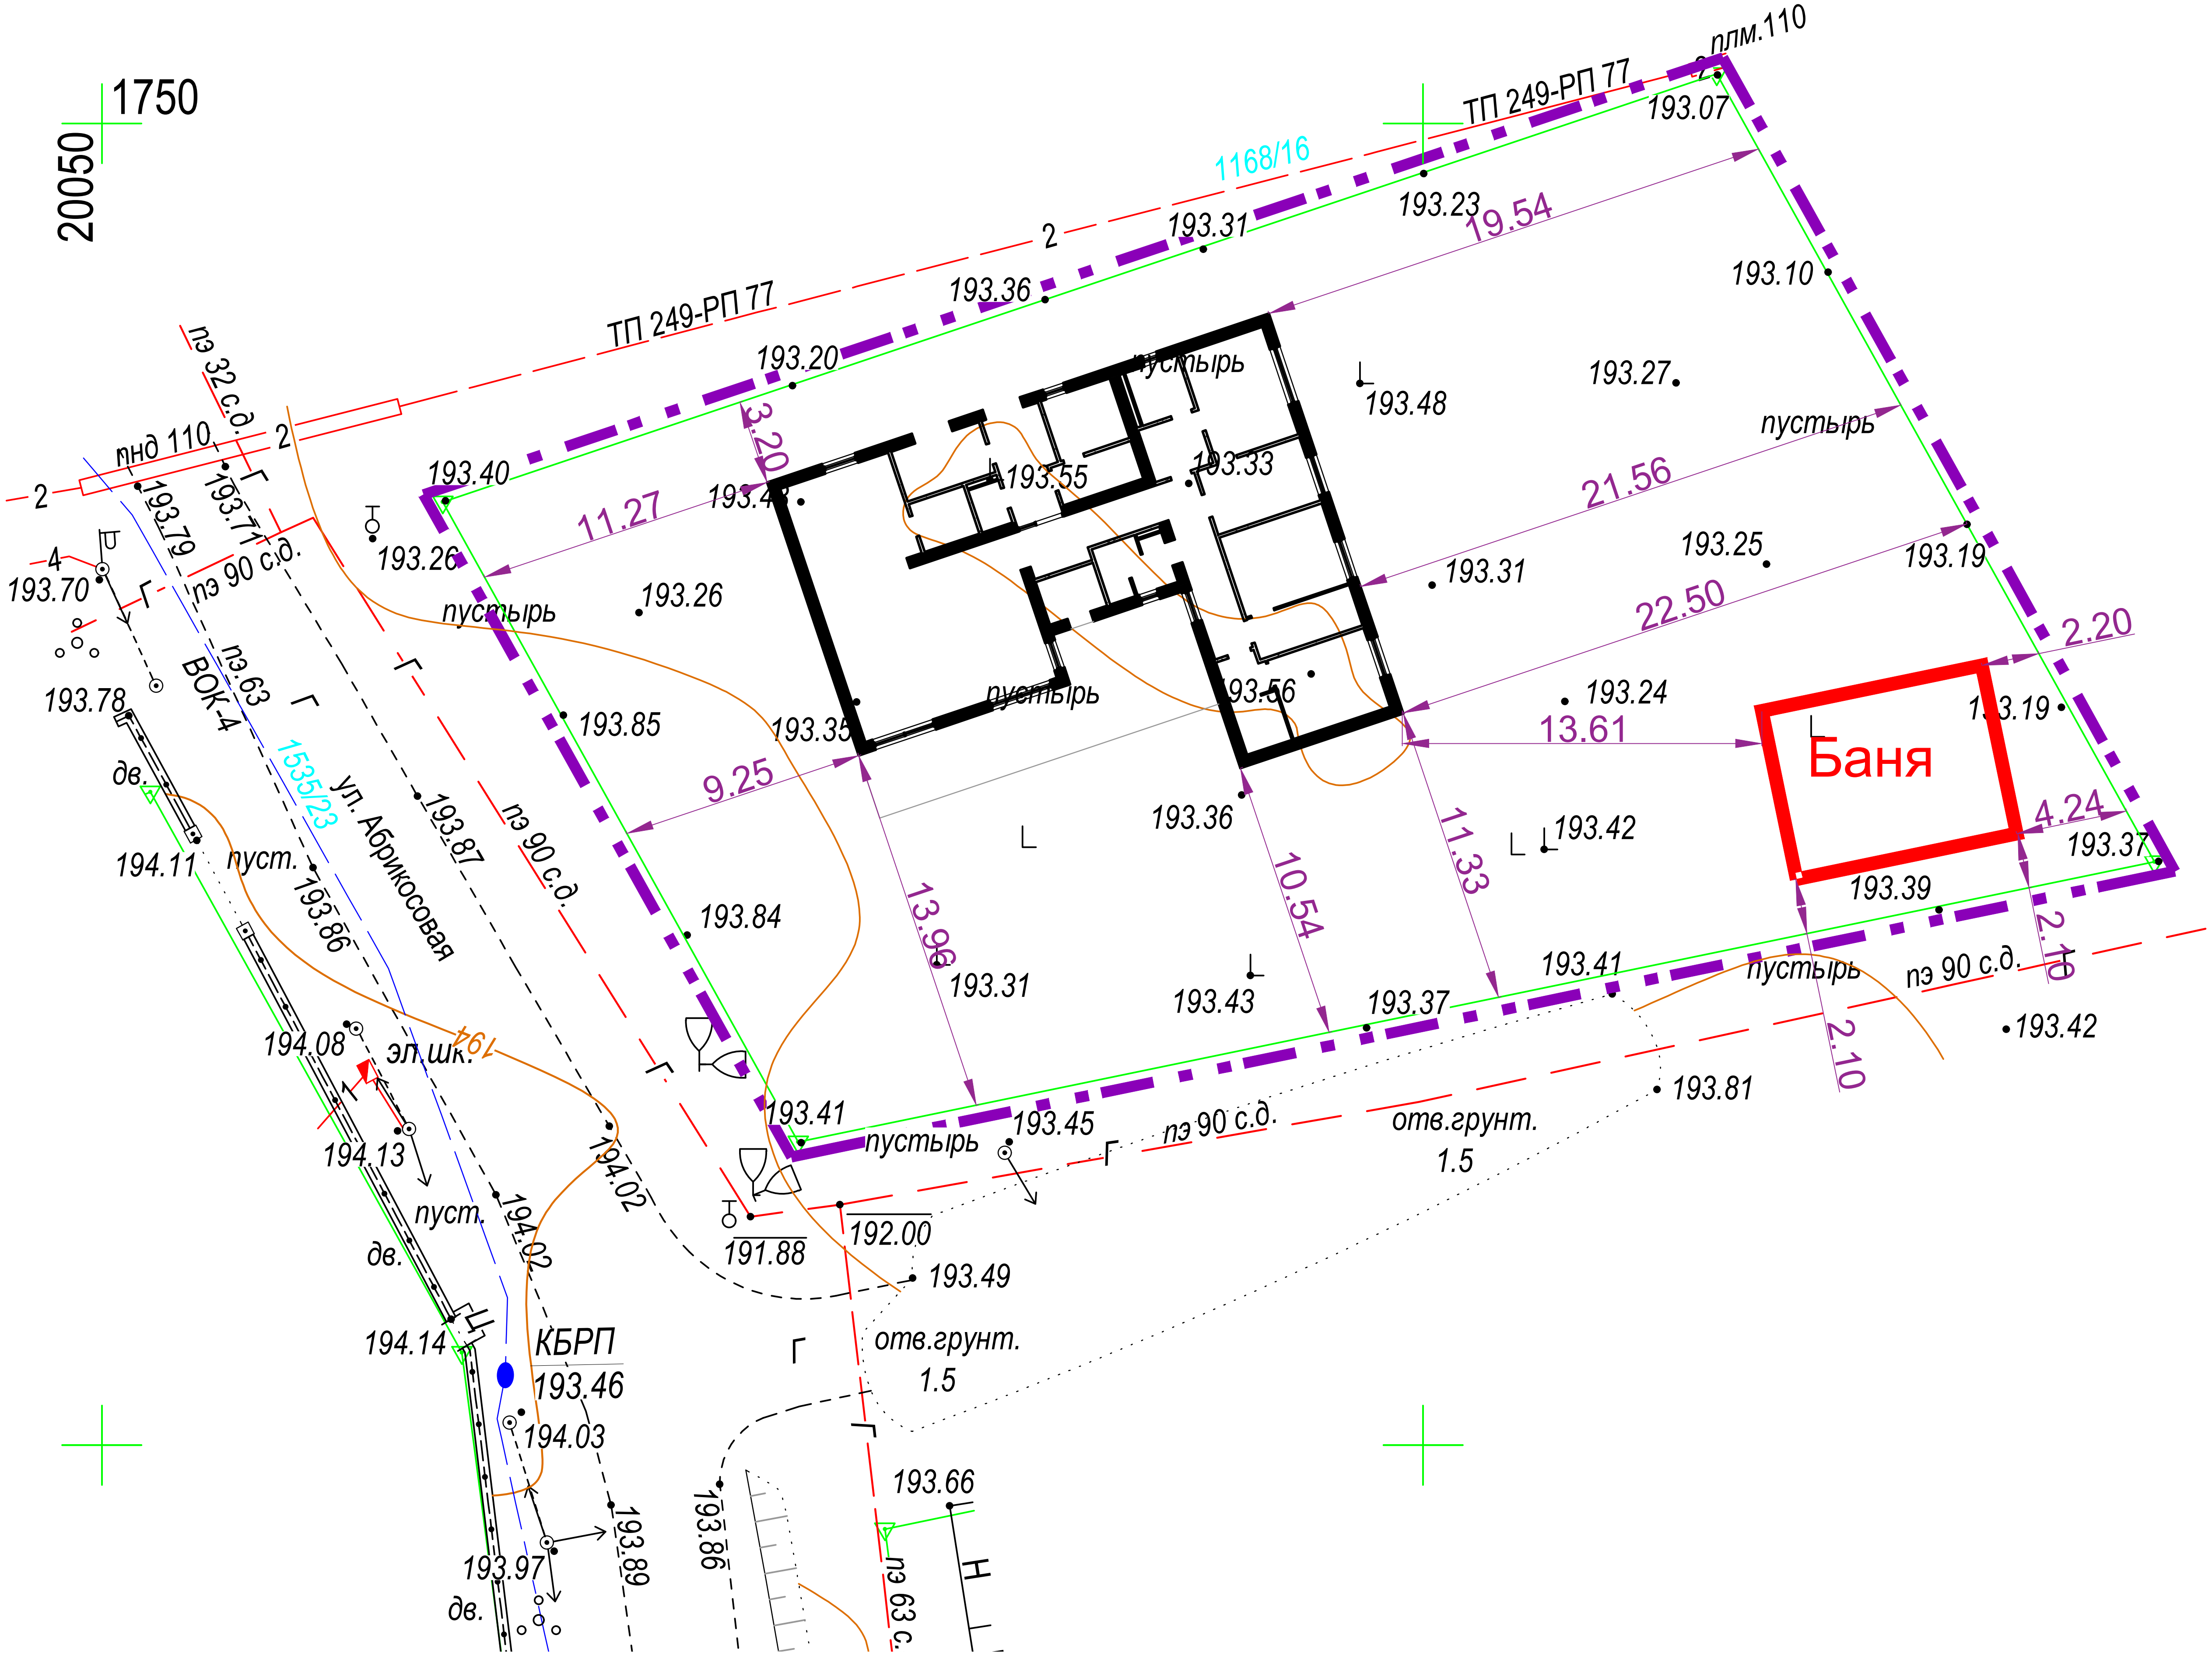
1750
20050
плм.110
ТП 249-РП 77
193.07
1168/16
193.23
19.54
193.31
2
193.36
ТП 249-РП 77
193.10
193.20
пустырь
193.48
193.27
3.20
193.55
193.33
пустырь
193.40
11.27
193.4
21.56
193.26
193.31
193.25
193.19
пустырь
193.26
22.50
2.20
пустырь
193.56
193.24
193.85
193.35
13.61
193.19
Баня
9.25
193.36
193.42
4.24
193.37
193.84
13.96
10.54
11.33
193.39
193.31
193.43
193.37
193.41
пустырь
пэ 90 с.д.
2.10
193.42
2.10
193.41
пустырь
193.45
пэ 90 с.д.
отв.грунт.
1.5
193.81
191.88
192.00
193.49
отв.грунт.
1.5
193.66
193.86
пэ 63 с.
Н
пз 32 с.д.
2
пнд 110
2
193.79
193.71
4
193.70
пэ 90 с.д.
193.78
ВОК-4
пэ 63
1535/23
ул. Абрикосовая
193.87
пэ 90 с.д.
дв.
194.11
пуст.
193.86
194.08
эл.шк.
194
194.13
194.02
пуст.
194.02
дв.
194.14
КБРП
193.46
194.03
193.97
дв.
193.89
Г